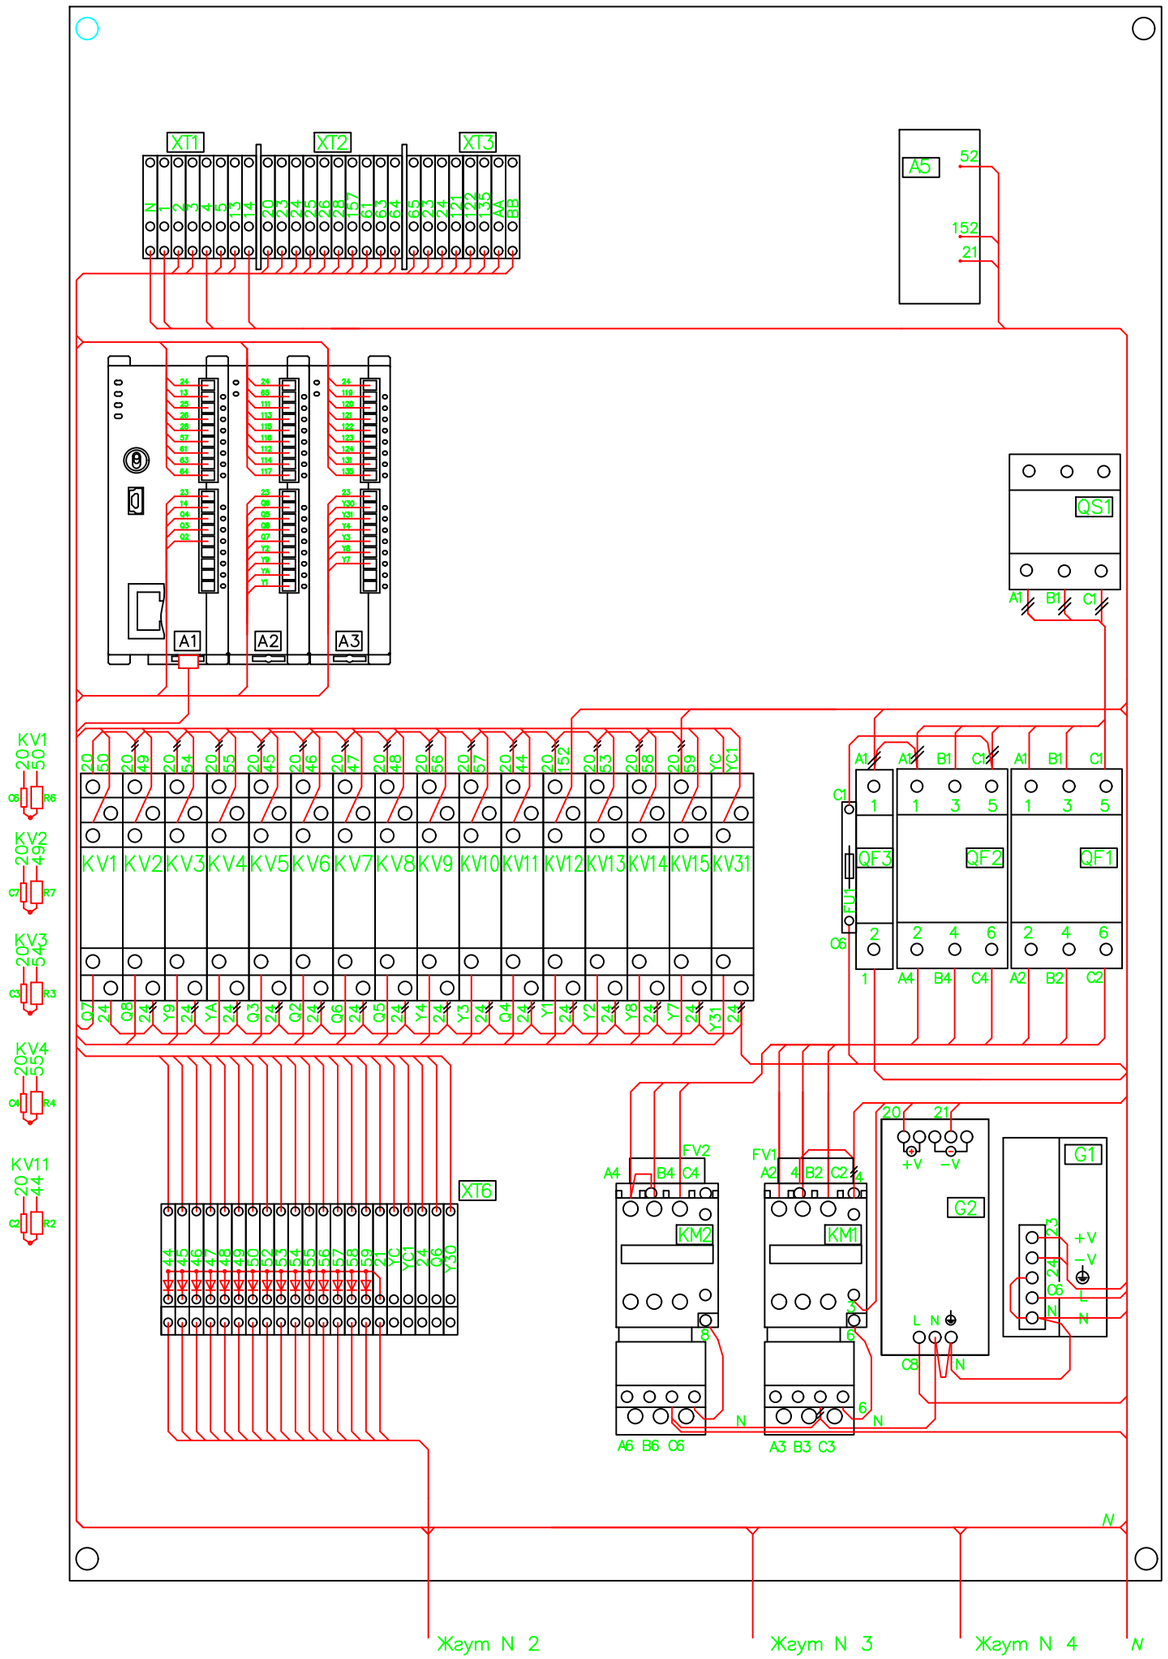


Таблица 1

Провод	Маркировка проводов	Диам. трубки мм
ПВ1 1,0 380	Все провода, кроме указанных ниже	3,5
ПВ1 2,5 380	20,21	4,0
ПВ1 6,0 380	A1, B1, C1, A2, B2, C2, A4, B4, C4	6,0

1. *Монтаж выполнить согласно данной схеме и чертежу Р–11 27.24.200–08 СБ. Технические требования к электромонтажу по ОСТ 92–0286–80.*
2. *Монтаж выполнить проводами, указанными в таблице 1.*
3. *На концы проводов надеть трубки ПВХ 305. ТВ–40 белые ГОСТ 19034–82 в соответствии с таблицей 1 длиной по 15мм с нанесенной на них согласно данной схеме маркировкой проводов. Маркировку на трубки наносить маркером черным "edding 140 S" шрифтом 3–Пр3 ГОСТ 26020–80.*
4. *Лудить и паять припоем Прв. КР2 ПОС–61 ГОСТ 21931–76 с применением флюса ФКСп ОСТ 4. ГО. 033. 200.*
5. *Жгуты вязать, крепить к панели с применением ленты монтажной ЛМ5 УХЛ2 ТУ 36–2699–85 и кнопок 3,5 МС УХЛ2 ГОСТ 17563–80.*

2	Зам.	ИИ 087–24		10.24
1	Зам.	ИИ 542–19		12.19
Изм.	Лист	N докум.	Подп.	Дата
Разраб.		Серебряков		05.18
Пров.		Порошин		
Т. контр.				
Утв.				


Р–11 27.24.200–08 Э4

Панель силовая
Схема электрическая соединений

Лит.	Масса	Масштаб
		1:5


Лист 1 Листов 2

РИФЕЙ
ЗАВОД СТРОЙТЕХНИКА

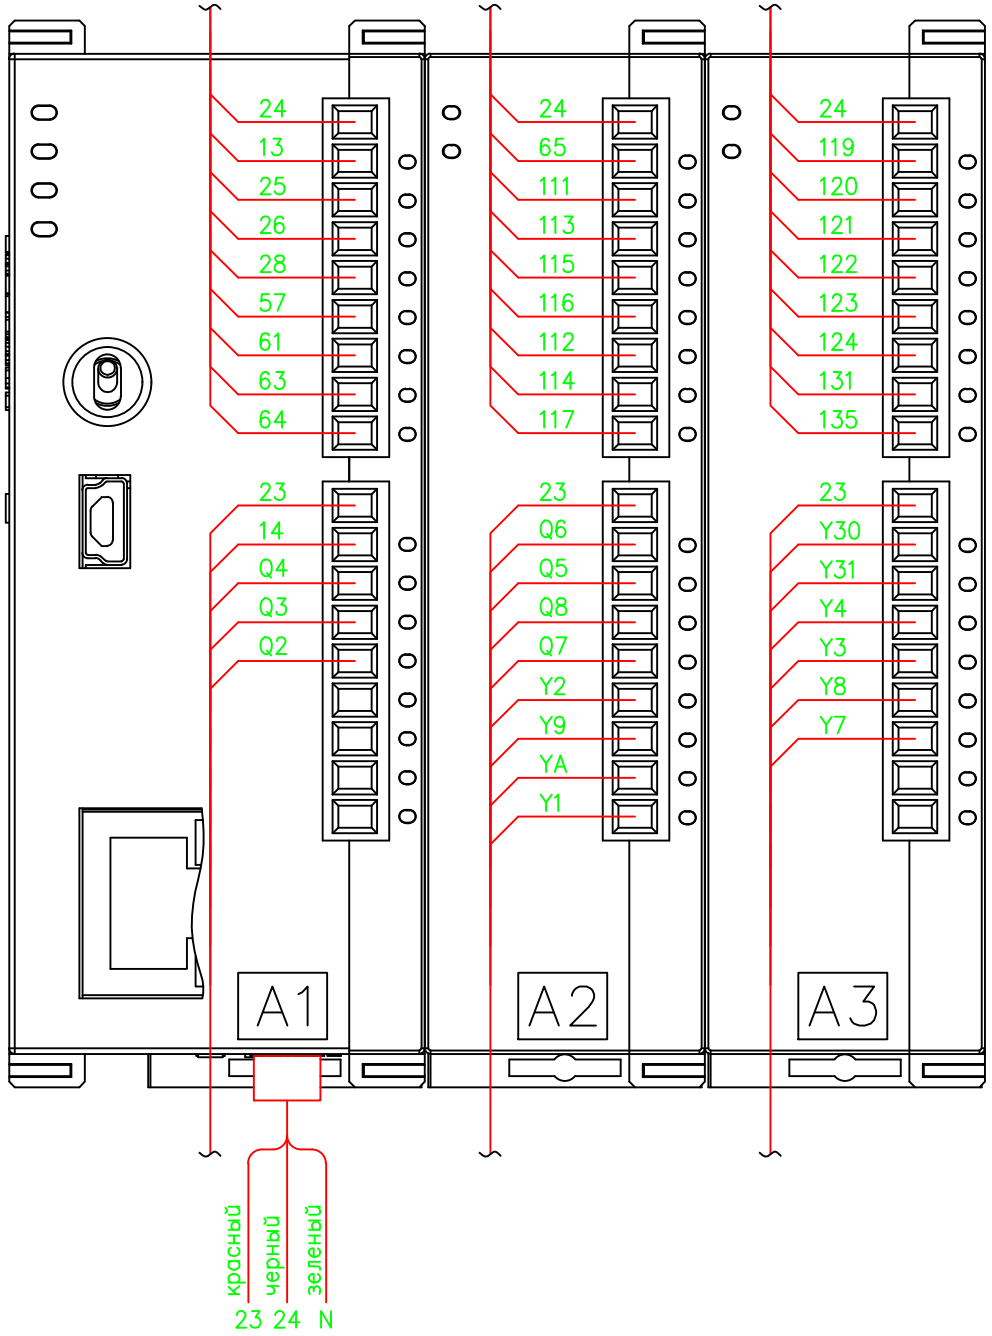

					Р–11 27.24.200–08 ЭЗ	Лист
1	Зам.	ИИ 542–19		12.19		2
Изм.	Лист	N докум.	Подп.	Дата		

Подключение проводников к розеткам на днище пульта

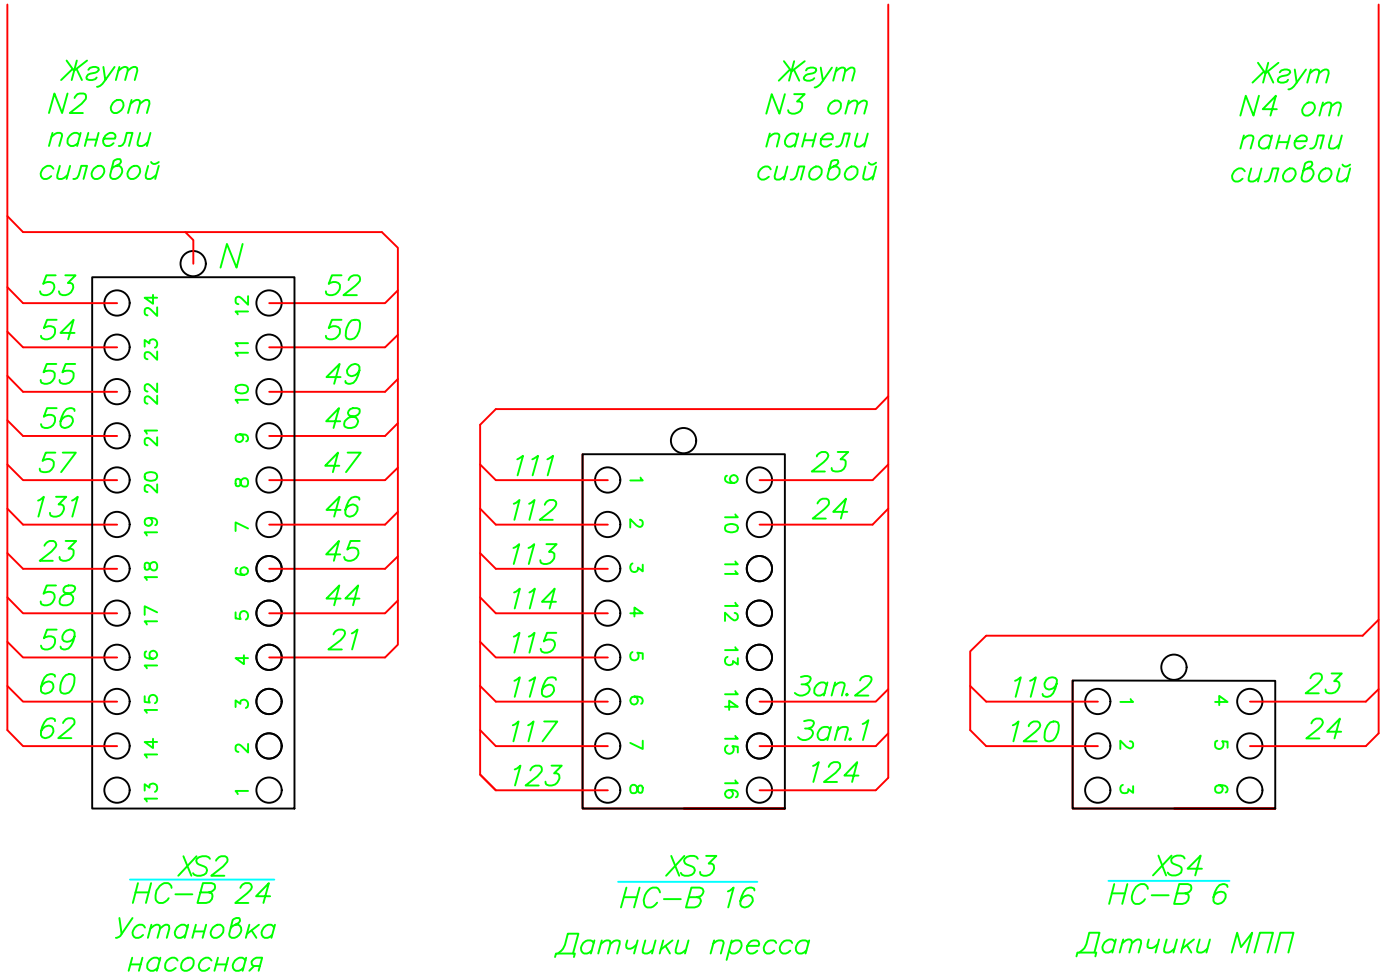

1	Зам.	ИИ 542–19		12.19	Р–11 27.24.200–08 Э4	Лист 3
Изм.	Лист	N докум.	Подп.	Дата		