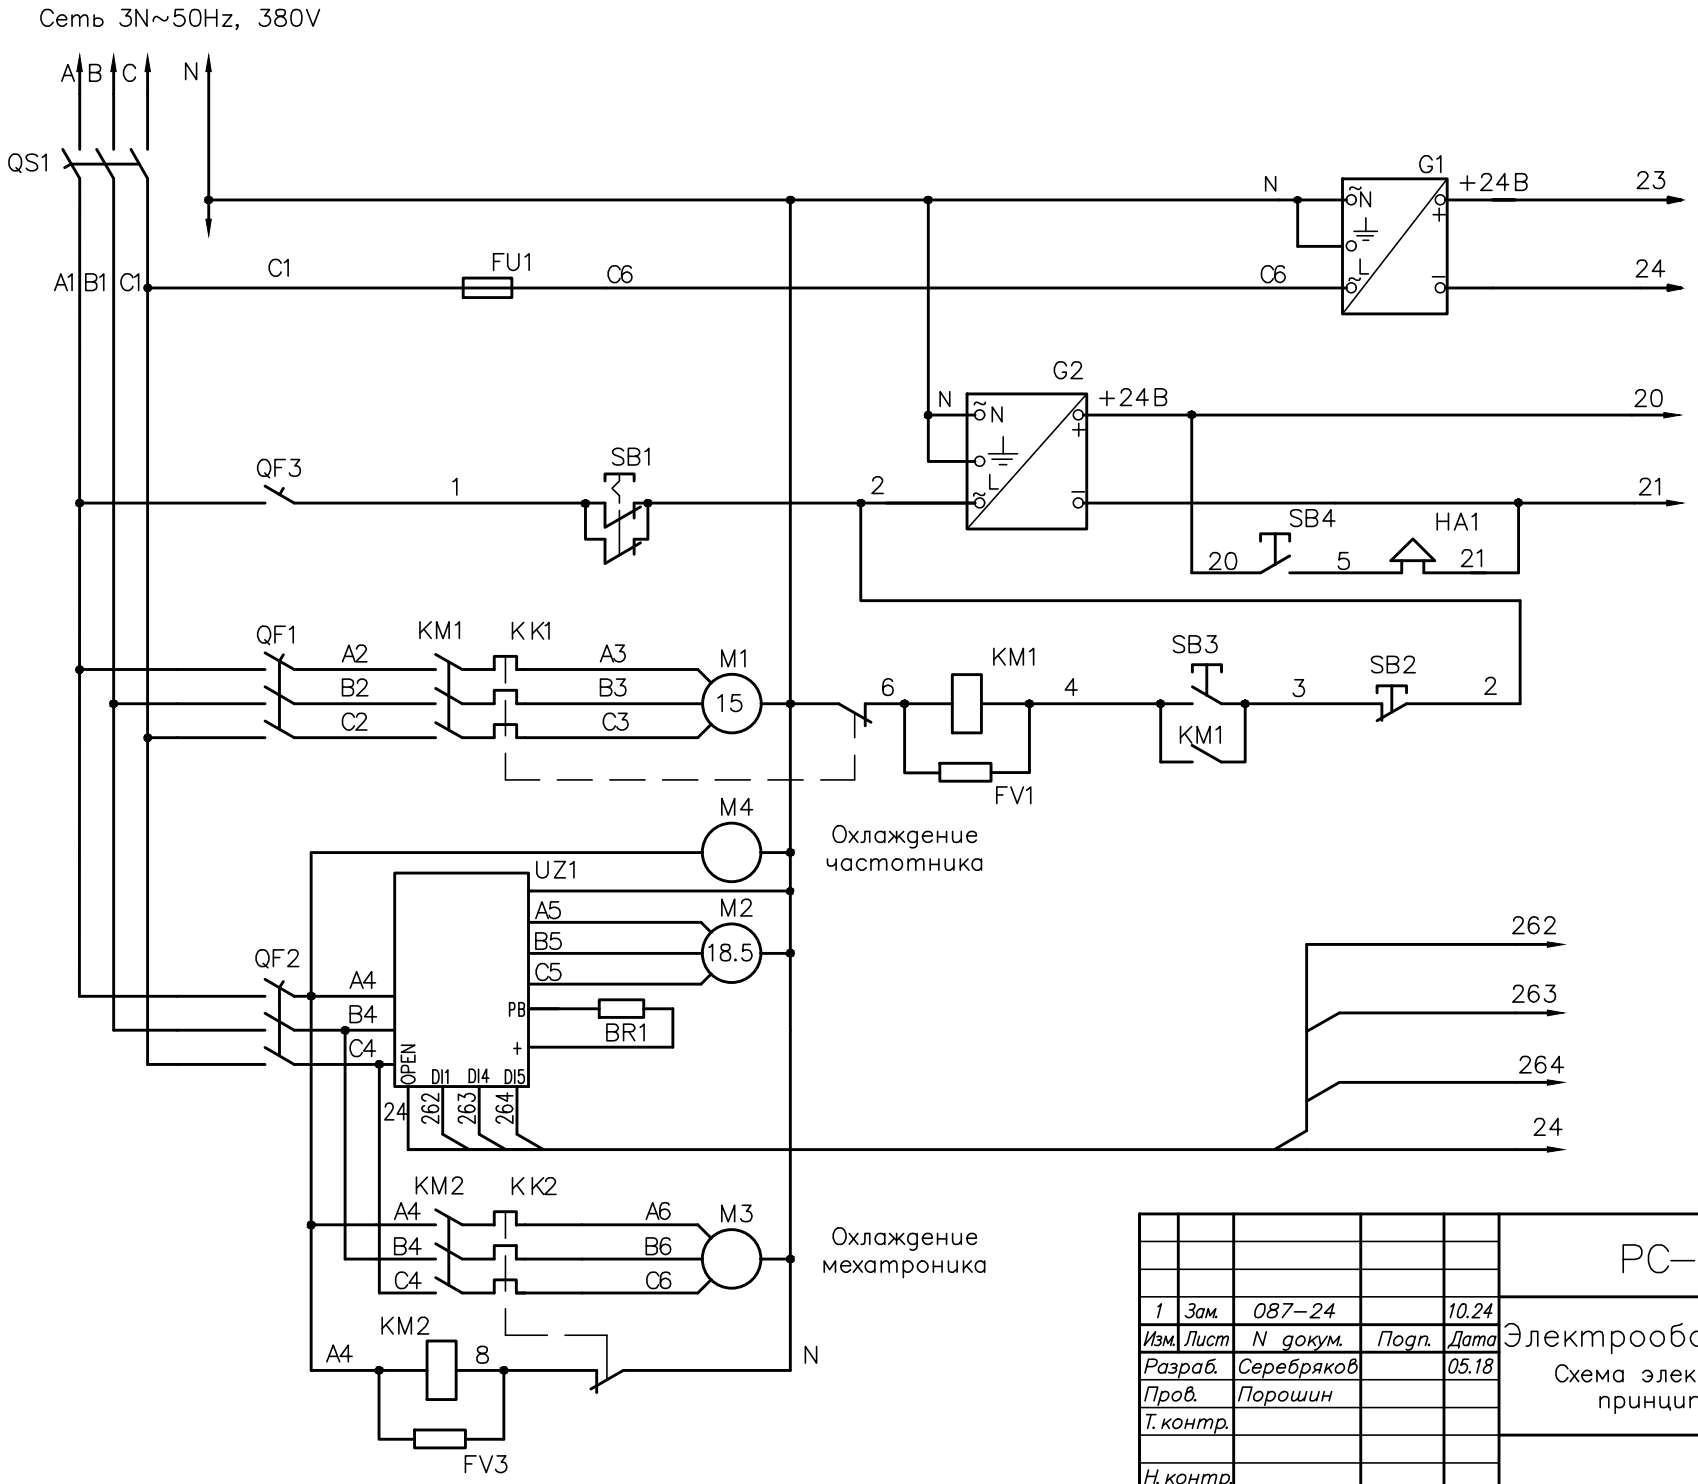


1	Зам.	087–24		10.24	
Изм.	Лист	N докум.	Подп.	Дата	
Разраб.		Серебряков		05.18	
Пров.		Порошин			
Т. контр.					
Н. контр.					
Утв.					

РС–5.02.24.000 Э3


Электрооборудование.


Схема электрическая принципиальная

Лит.	Масса	Масштаб


Лист 1 Листов 5

РИФЕЙ
ЗАВОД СТРОЙТЕХНИКА

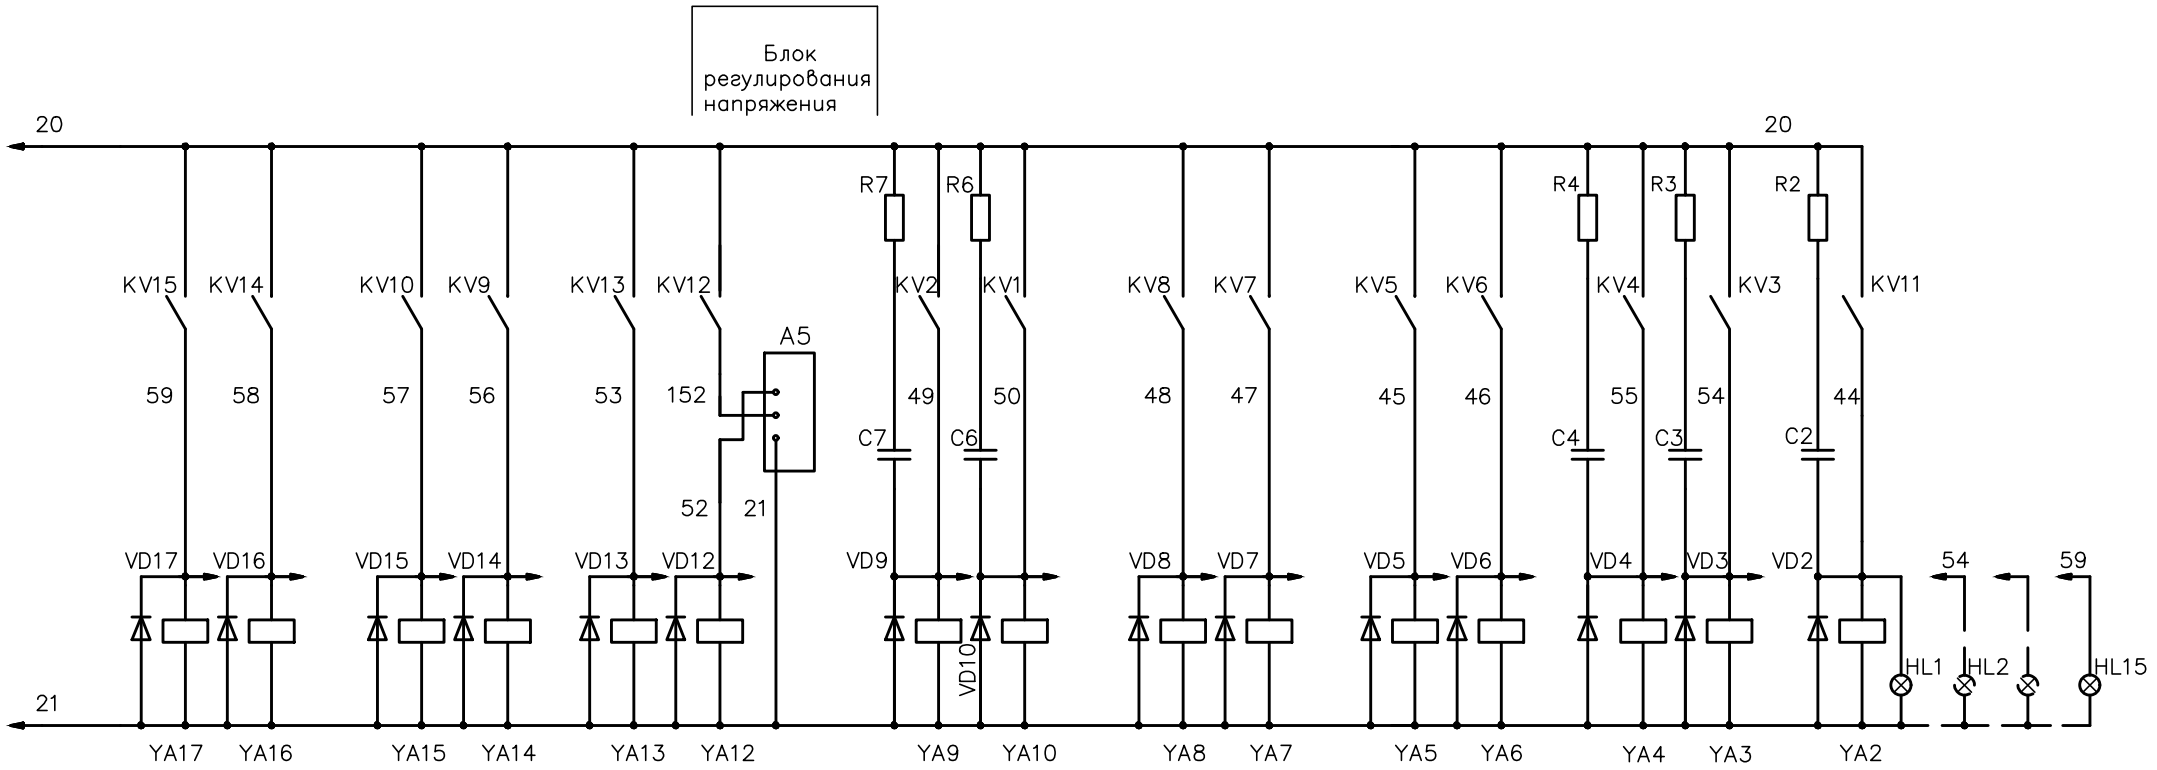

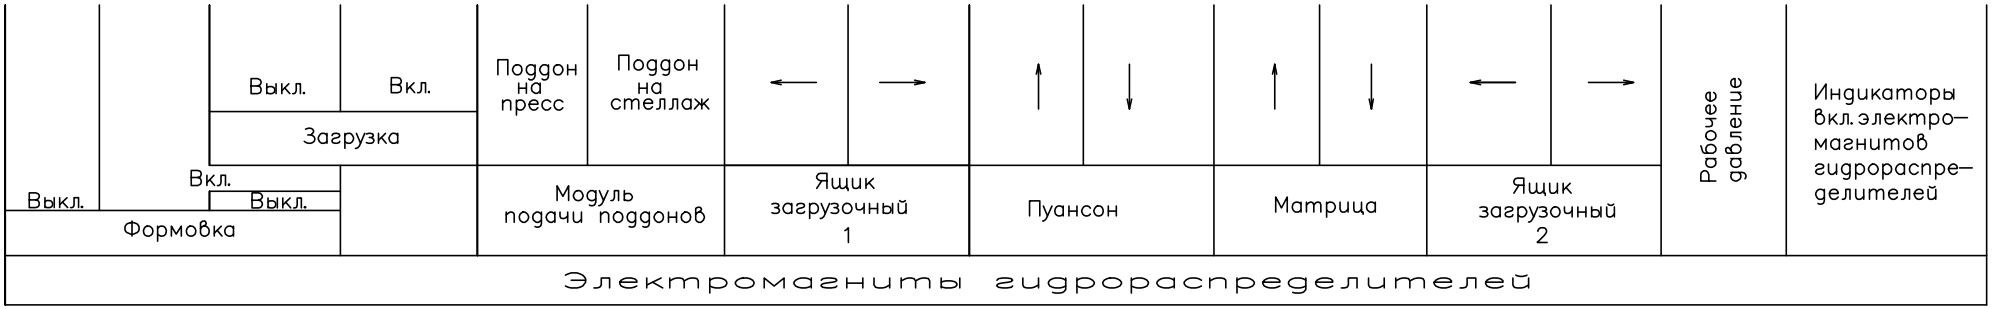


Изм.	Лист	N докум.	Подп.	Дата	РС–5.02.24.000 ЭЗ	Лист 2

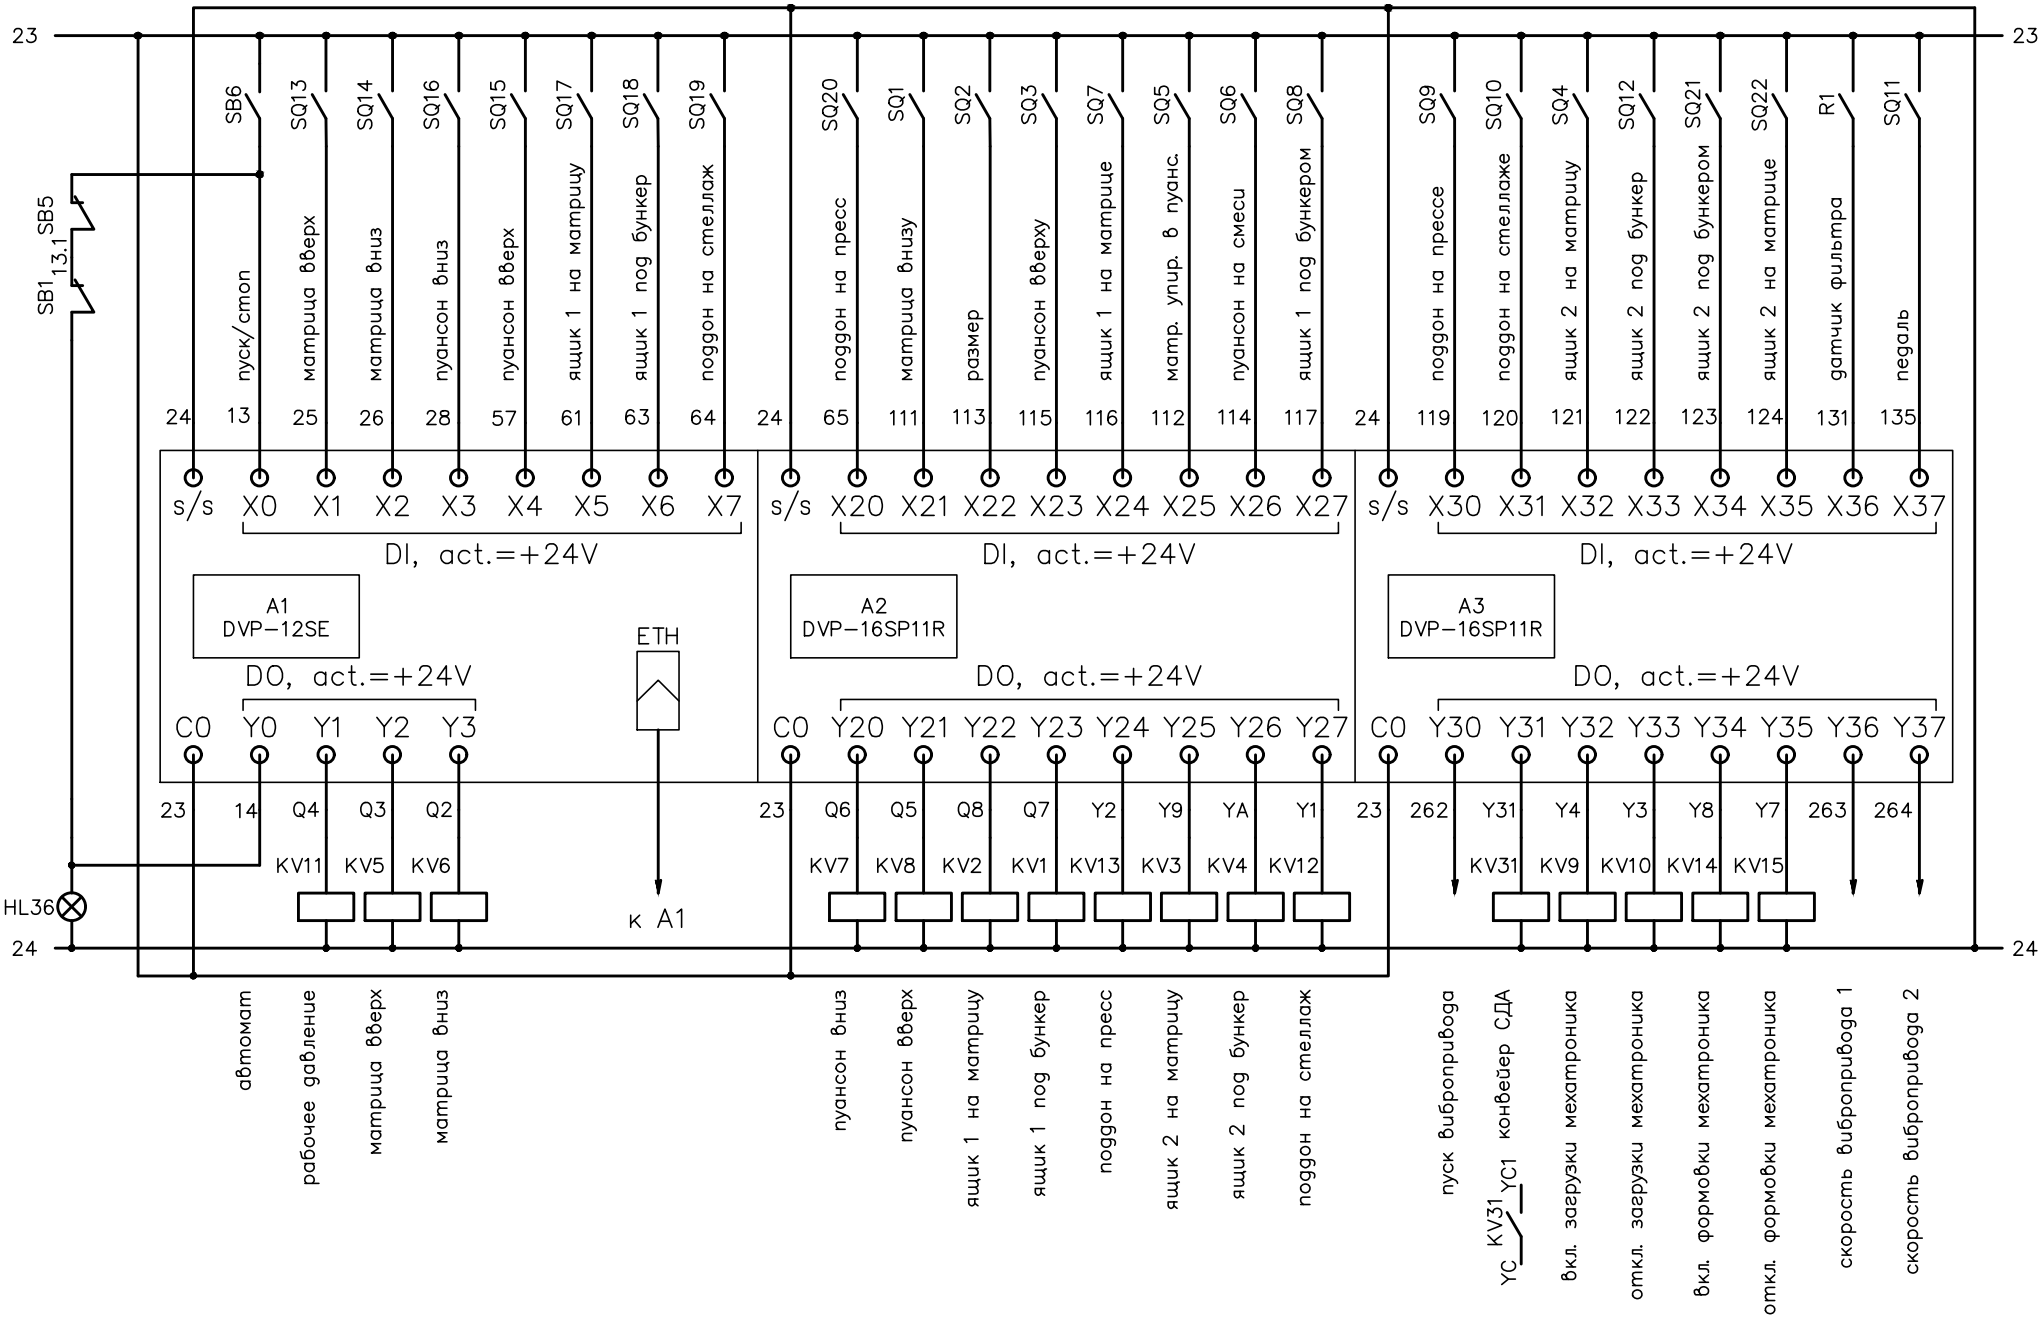


1	Зам.	087-24		10.24	
Изм.	Лист	N докум.	Подп.	Дата	


РС-5.02.24.000 Э3

Лист 3

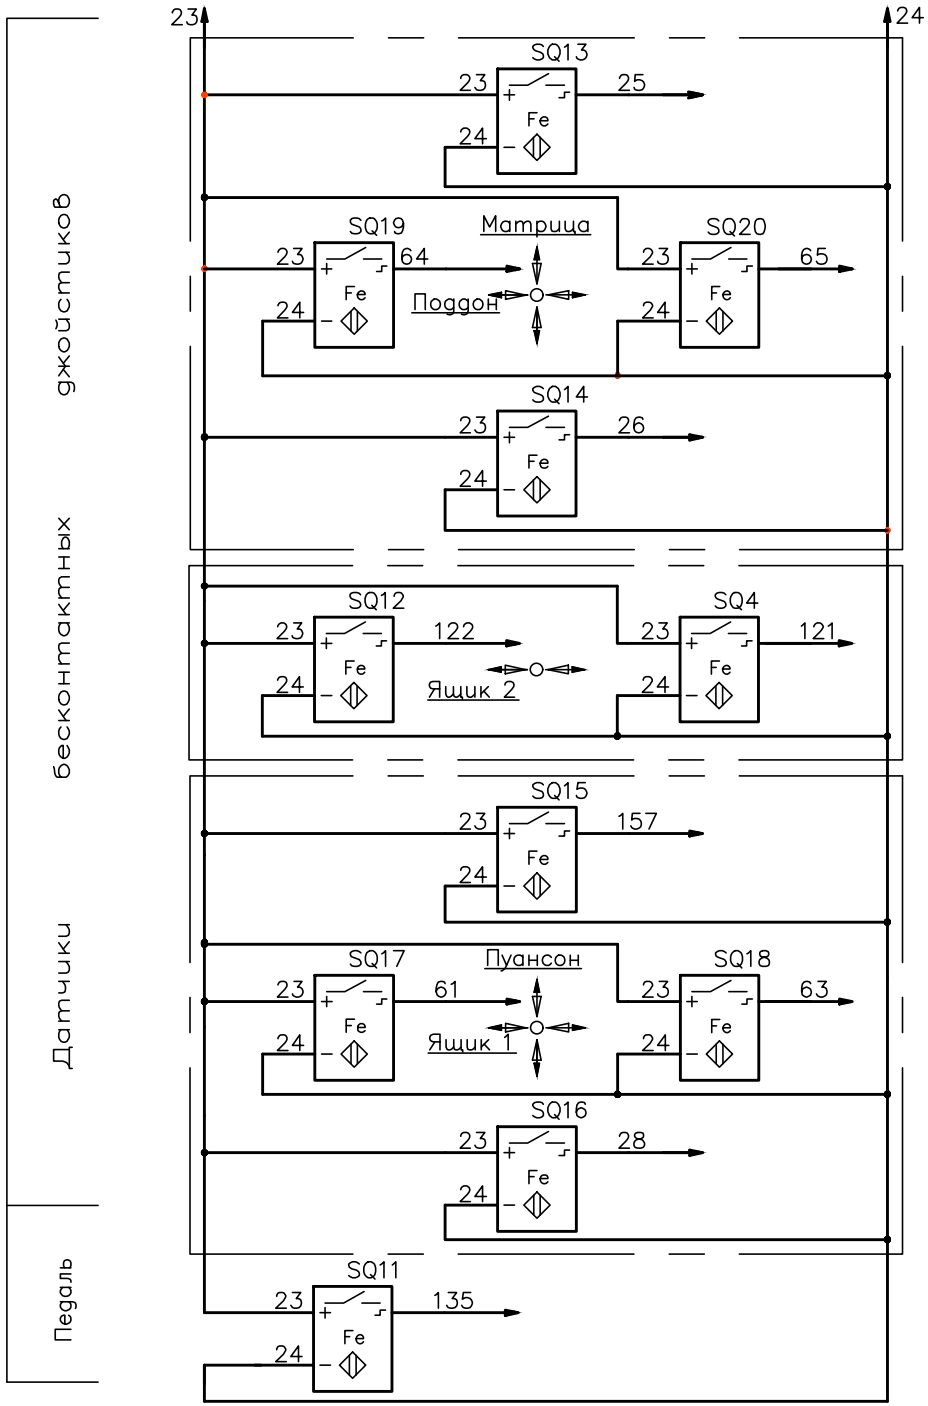


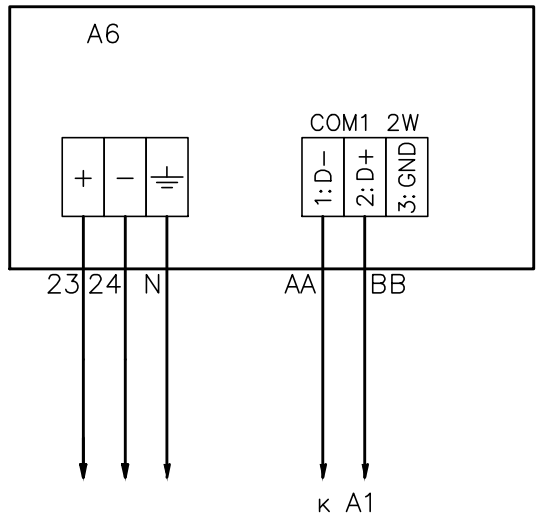

Панель оператора

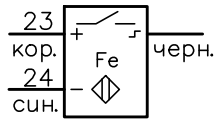

Изм.	Лист	N докум.	Подп.	Дата	РС–5.02.24.000 ЭЗ	Лист 4

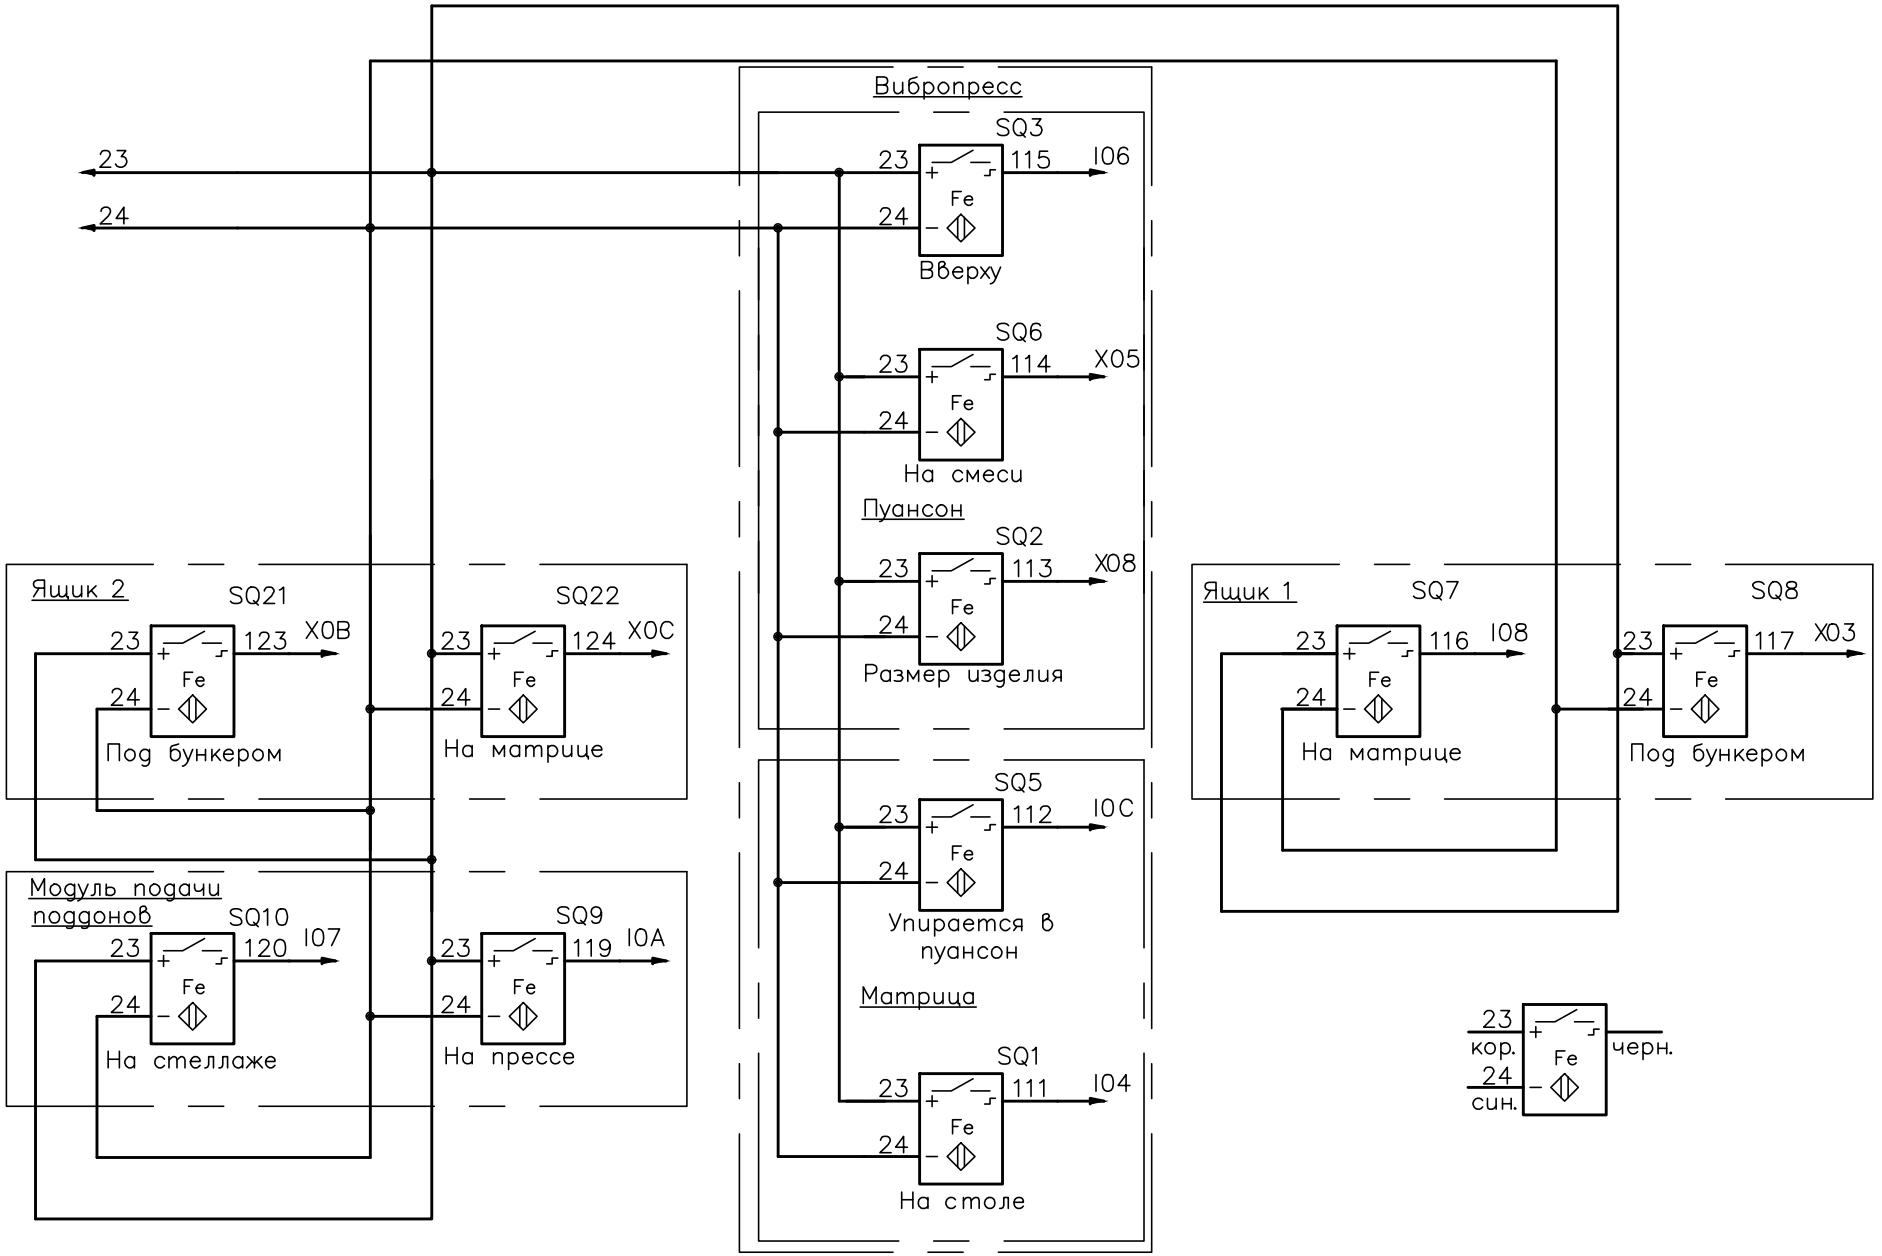

Датчики положения исполнительных узлов пресса

Изм.	Лист	N документа	Подпись	Дата	РС–5.02.24.000 Э3	Лист 5